


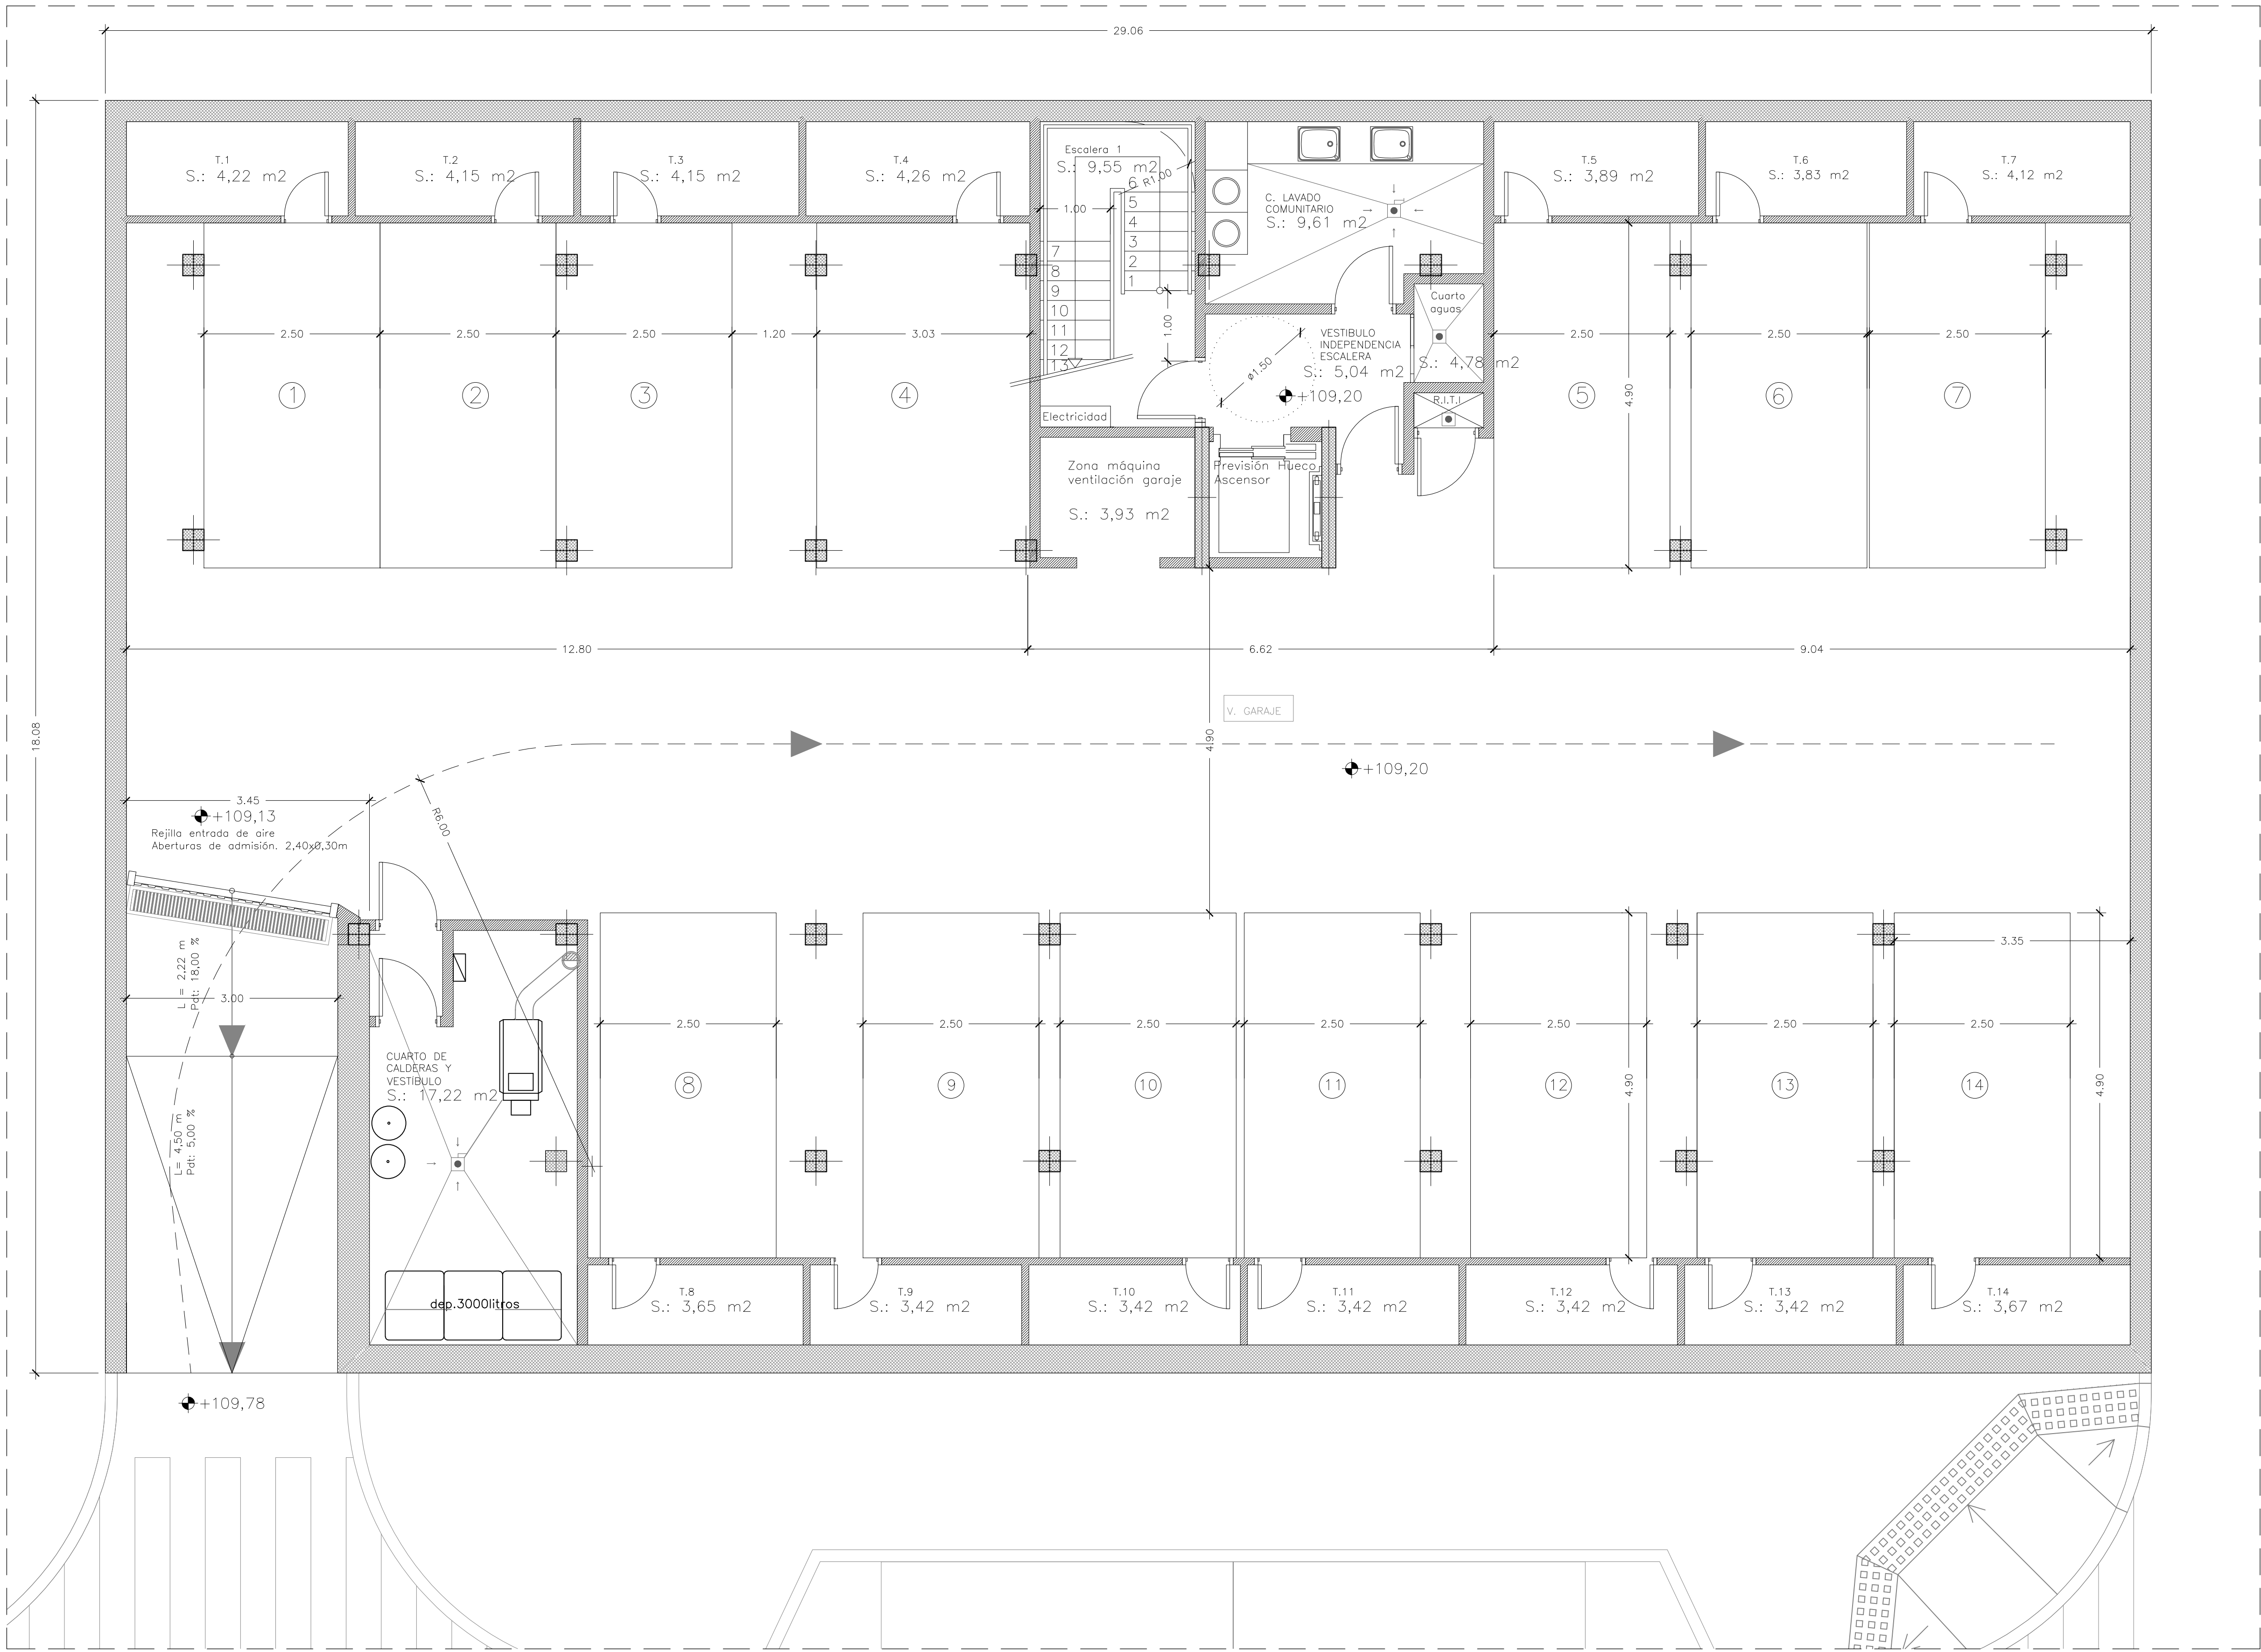

CUADROS DE SUPERFICIES CONSTRUIDAS

PLANTA BAJA	SUP.CONSTRUIDA		
	computable	no computable	total
Zonas comunes	44,80 m2	2,00 m2	46,80 m2
Vivienda A	42,71 m2	0,00 m2	42,71 m2
Vivienda B	55,32 m2	0,00 m2	55,32 m2
Vivienda C	54,30 m2	0,00 m2	54,30 m2
Vivienda D	55,05 m2	0,00 m2	55,05 m2
Vivienda E	53,03 m2	0,00 m2	53,03 m2
Total planta baja	305,21 m2	2,00 m2	307,21 m2

RESUMEN SUPERFICIE CONSTRUIDA			
	computable	no computable	total
Planta baja	305,21 m2	2,00 m2	307,21 m2
Planta primera	307,21 m2	8,60 m2	315,81 m2
Planta bajocubierta	197,58 m2	7,02 m2	204,60 m2
Planta semisótano	--- m2	500,41 m2	500,41 m2
Total construida	810,00 m2	518,03 m2	1328,03 m2

CUMPLIMIENTO URBANISTICO. ZONA-A3. BLOQUE 3			
	proyecto	estudio de detalle	
Edificabilidad	810,00 m2t	810,00 m2t	
Sup. ocupación	314,30 m2	334,86 m2	
Densidad	12 viv.	14 viv.	

PS

CUADROS DE SUPERFICIES ÚTILES

ZONAS COMUNES	SUPERFICIE
Vestibulo independencia escaleras	5,04 m2
Hueco escalera	9,55 m2
Cuarto de lavado comunitario	9,61 m2
Hueco ascensor	2,73 m2
Cuarto de Aguas	4,78 m2
Cuarto de Caldera y Vest. Ind.	17,22 m2
Zona maq ventilación garaje	3,93 m2
Total sup. útil zonas comunes	52,86 m2

USO GARAJE	SUPERFICIE
Pasos y calles	181,20 m2
Plazas de garaje	171,50 m2
Total sup. útil uso garaje	352,70 m2

USO TRASTEROS	SUPERFICIE
Trastero 1	4,22 m2
Trastero 2	4,15 m2
Trastero 3	4,15 m2
Trastero 4	4,26 m2
Trastero 5	3,89 m2
Trastero 6	3,83 m2
Trastero 7	4,12 m2
Trastero 8	3,65 m2
Trastero 9	3,42 m2
Trastero 10	3,42 m2
Trastero 11	3,42 m2
Trastero 12	3,42 m2
Trastero 13	3,42 m2
Trastero 14	3,67 m2
Total sup. útil trasteros	53,04 m2

TOTAL ÚTIL SEMISÓTANO	SUPERFICIE
Zonas comunes	52,86 m2
Uso garaje	352,70 m2
Trasteros	53,04 m2
Total sup. útil semisótano	458,60 m2