


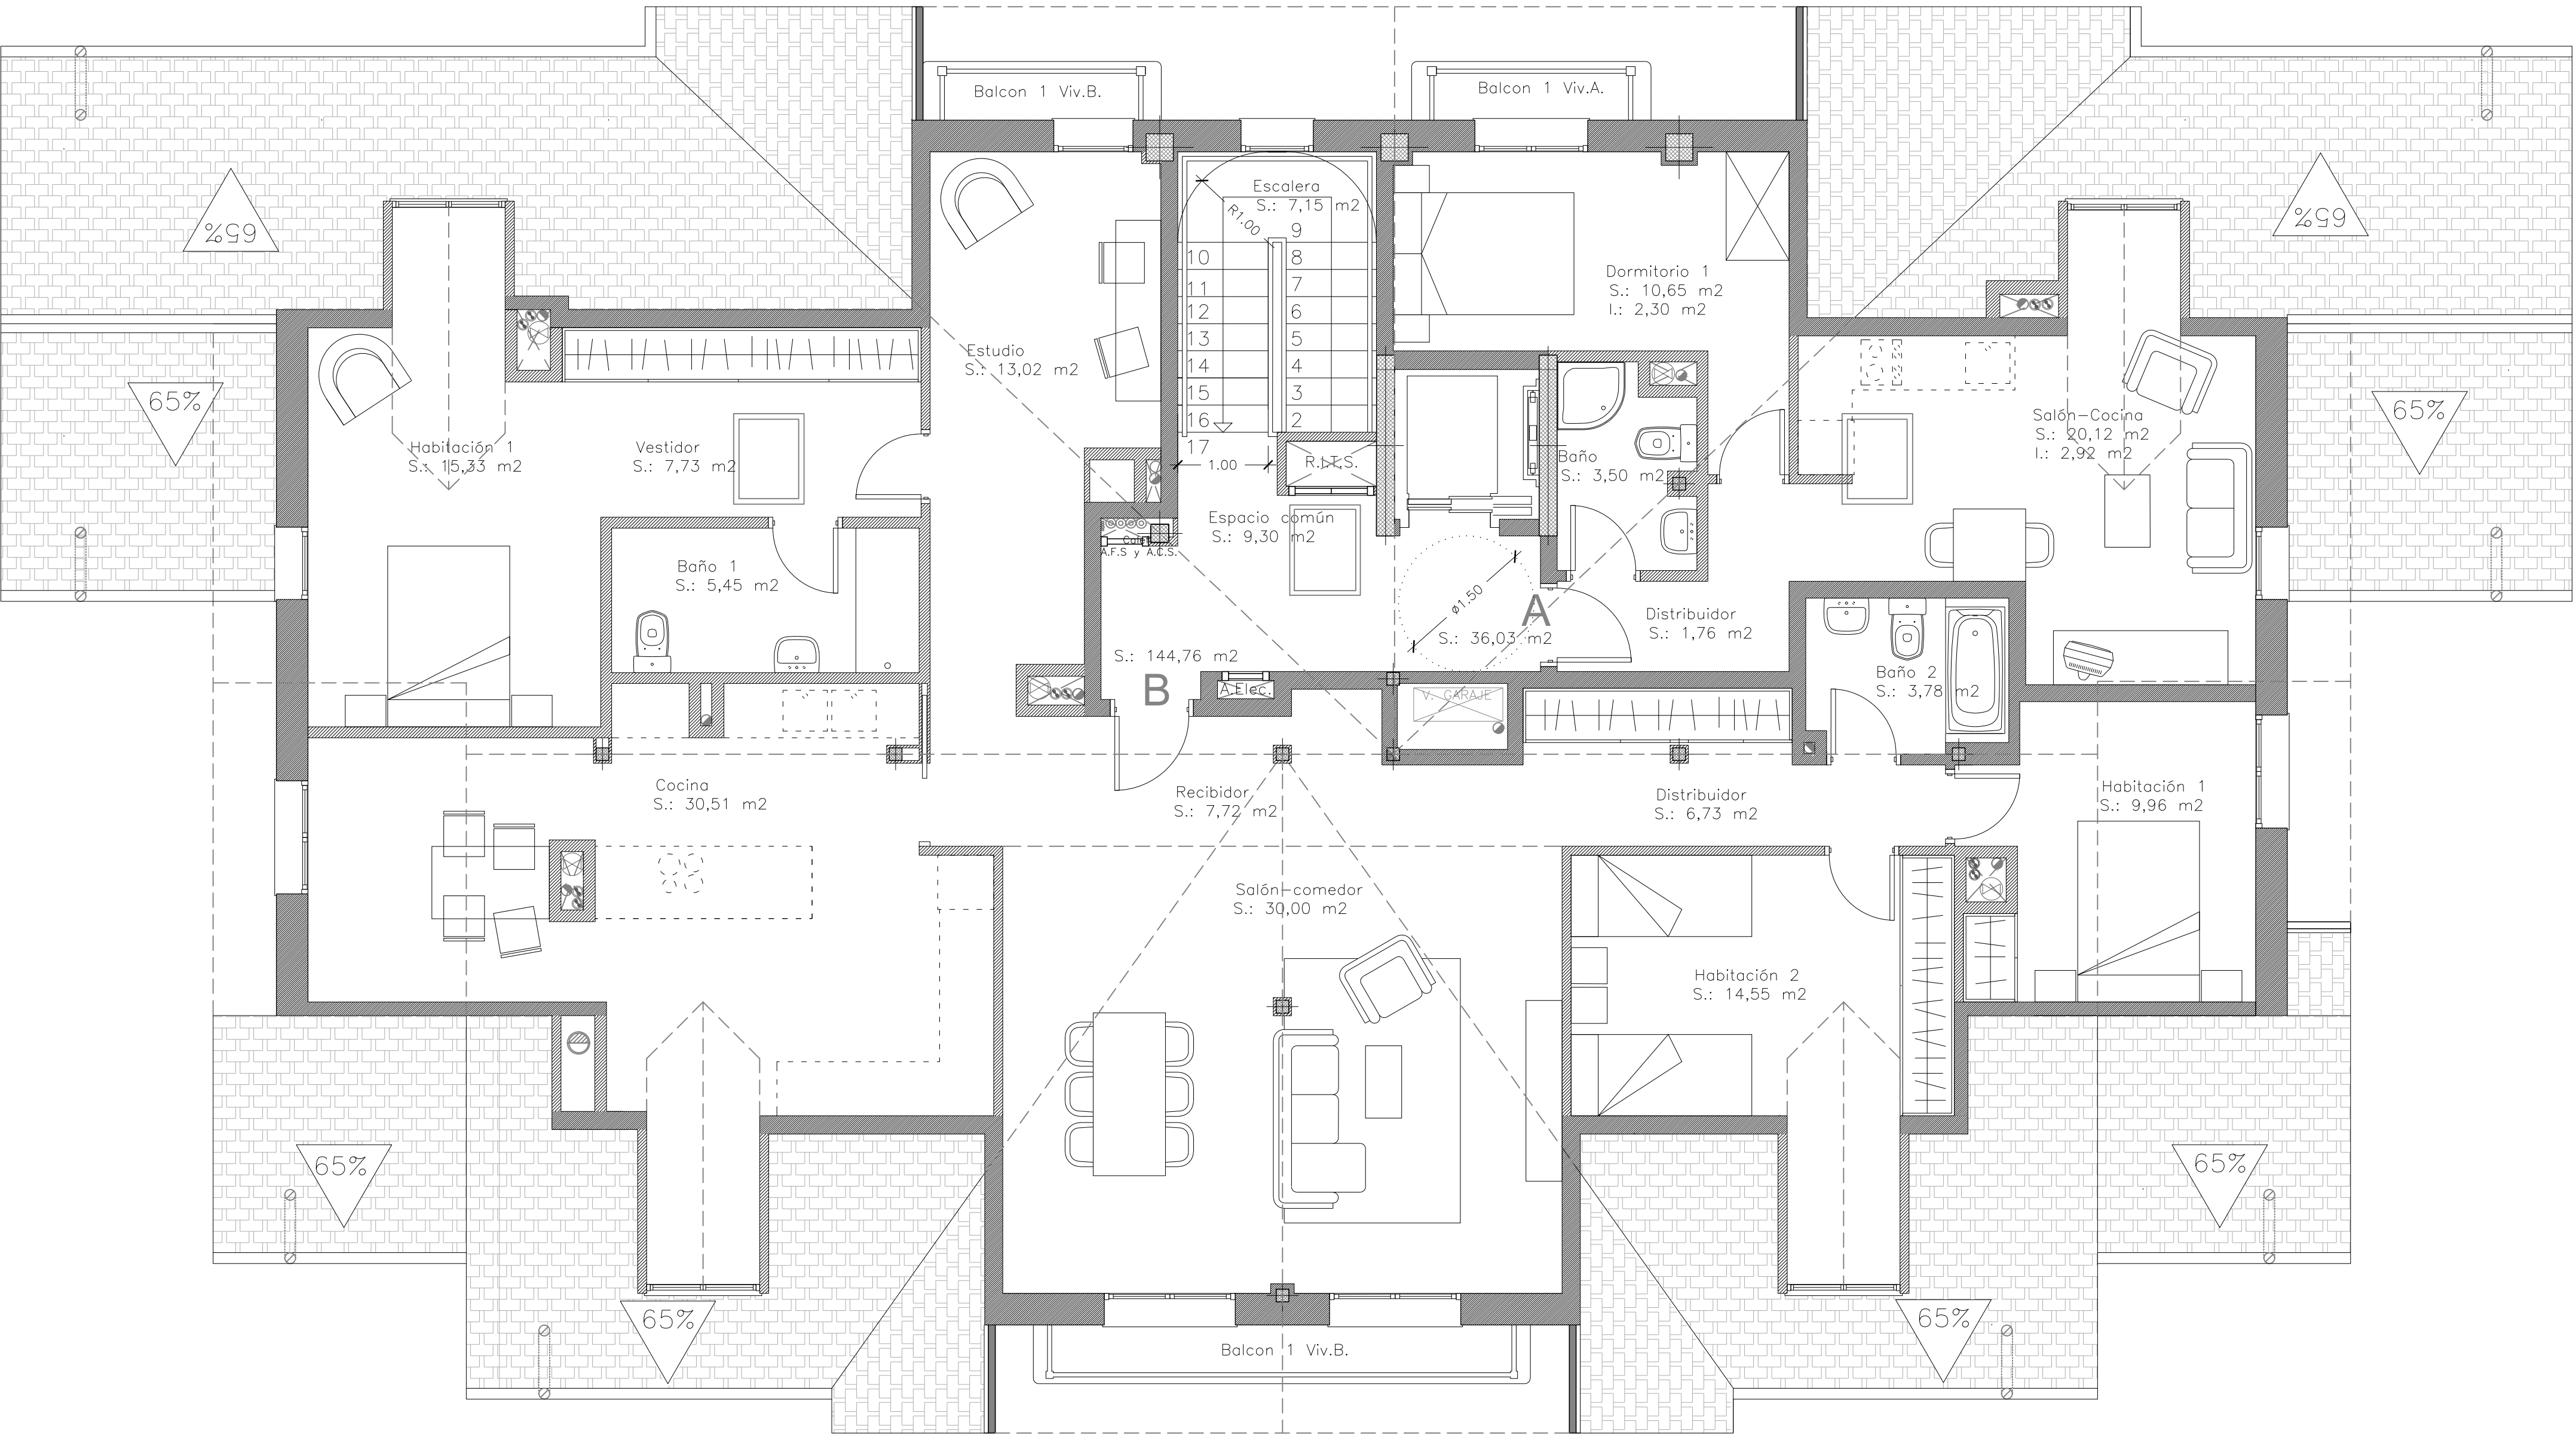

CUADROS DE SUPERFICIES ÚTILES POR VIVIENDA

VIVIENDA A	SUPERFICIE	VIVIENDA D	SUPERFICIE
Salón-cocina	20,03 m2	Salón-cocina	20,30 m2
Dormitorio 1	10,10 m2	Dormitorio 1	10,20 m2
Dormitorio 2	7,14 m2	Dormitorio 2	7,90 m2
Baño	3,52 m2	Baño	3,57 m2
Vestíbulo	1,58 m2	Vestíbulo	2,62 m2
Pasillo	2,64 m2	Pasillo	2,55 m2
Total sup. útil cerrada	45,01 m2	Total sup. útil cerrada	47,14 m2
Total sup. útil	45,01 m2	Balcón	1,72 m2
		Total sup. útil	48,86 m2

VIVIENDA B	SUPERFICIE	VIVIENDA E	SUPERFICIE
Salón-cocina	20,83 m2	Salón-cocina	20,05 m2
Dormitorio 1	10,20 m2	Dormitorio 1	10,00 m2
Dormitorio 2	7,66 m2	Dormitorio 2	6,36 m2
Baño	3,58 m2	Baño	3,50 m2
Vestíbulo	1,56 m2	Vestíbulo	1,29 m2
Pasillo	3,97 m2	Pasillo	3,12 m2
Total sup. útil cerrada	47,80 m2	Total sup. útil cerrada	44,32 m2
Balcón	1,72 m2	Balcón	1,72 m2
Total sup. útil	49,52 m2	Total sup. útil	46,04 m2

VIVIENDA C	SUPERFICIE	ZONAS COMUNES	SUPERFICIE
Salón-cocina	24,78 m2	Cuarto de limpieza	2,25 m2
Dormitorio 1	12,61 m2	Espacio común	15,22 m2
Baño	5,62 m2	Escalera	7,15 m2
Pasillo	1,51 m2		
Total sup. útil cerrada	44,52 m2	Total sup. útil z.comun	24,62 m2
Balcón 1	1,72 m2		
Balcón 2	1,72 m2		
Total sup. útil	47,96 m2		

CUADROS DE SUPERFICIES CONSTRUIDAS

PLANTA BAJOCUBIERTA	SUP.CONSTRUIDA	
Zonas comunes	computable no computable total	
Vivienda A	13,08 m2 0,00 m2 13,08 m2	
Vivienda B	41,82 m2 1,72 m2 43,54 m2	
Vivienda C	142,68 m2 5,37 m2 147,98 m2	
Total planta bajocubierta	197,58 m2 7,02 m2 204,60 m2	

RESUMEN SUPERFICIE CONSTRUIDA			
	computable no computable total		
Planta baja	305,21 m2 2,00 m2 307,21 m2		
Planta primera	307,21 m2 8,60 m2 315,81 m2		
Planta bajocubierta	197,58 m2 7,02 m2 204,60 m2		
Planta semisótano	----- m2 500,41 m2 500,41 m2		
Total construida	810,00 m2 518,03 m2 1328,03 m2		

CUMPLIMIENTO URBANÍSTICO. ZONA-A3. BLOQUE 3		
	proyecto estudio de detalle	
Edificabilidad	810,00 m2t 810,00 m2t	
Sup. ocupación	314,30 m2 334,86 m2	
Densidad	12 viv. 14 viv.	